



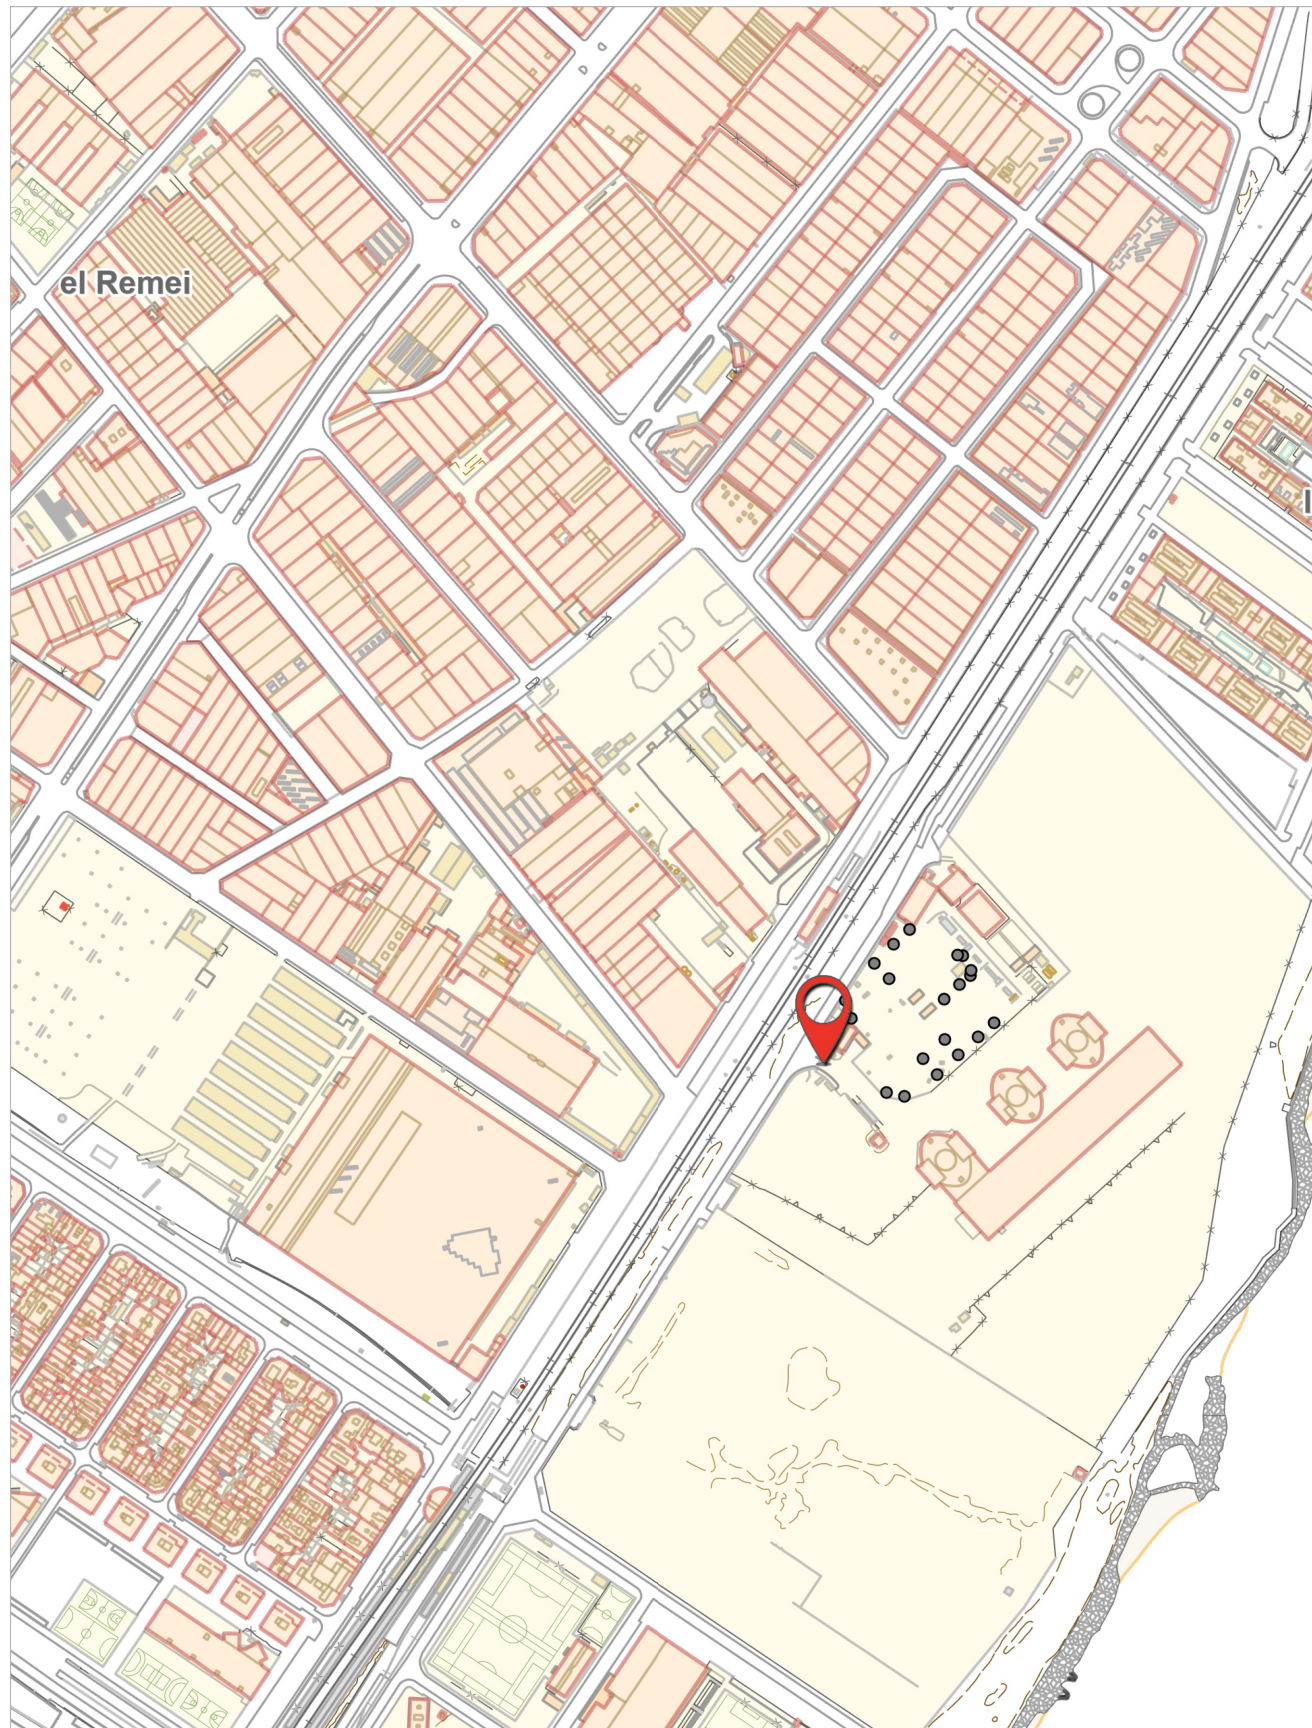

EMPLAÇAMENT ESCALA 1:5000
 REFERÈNCIA CADASTRAL: 6164301DF3866C

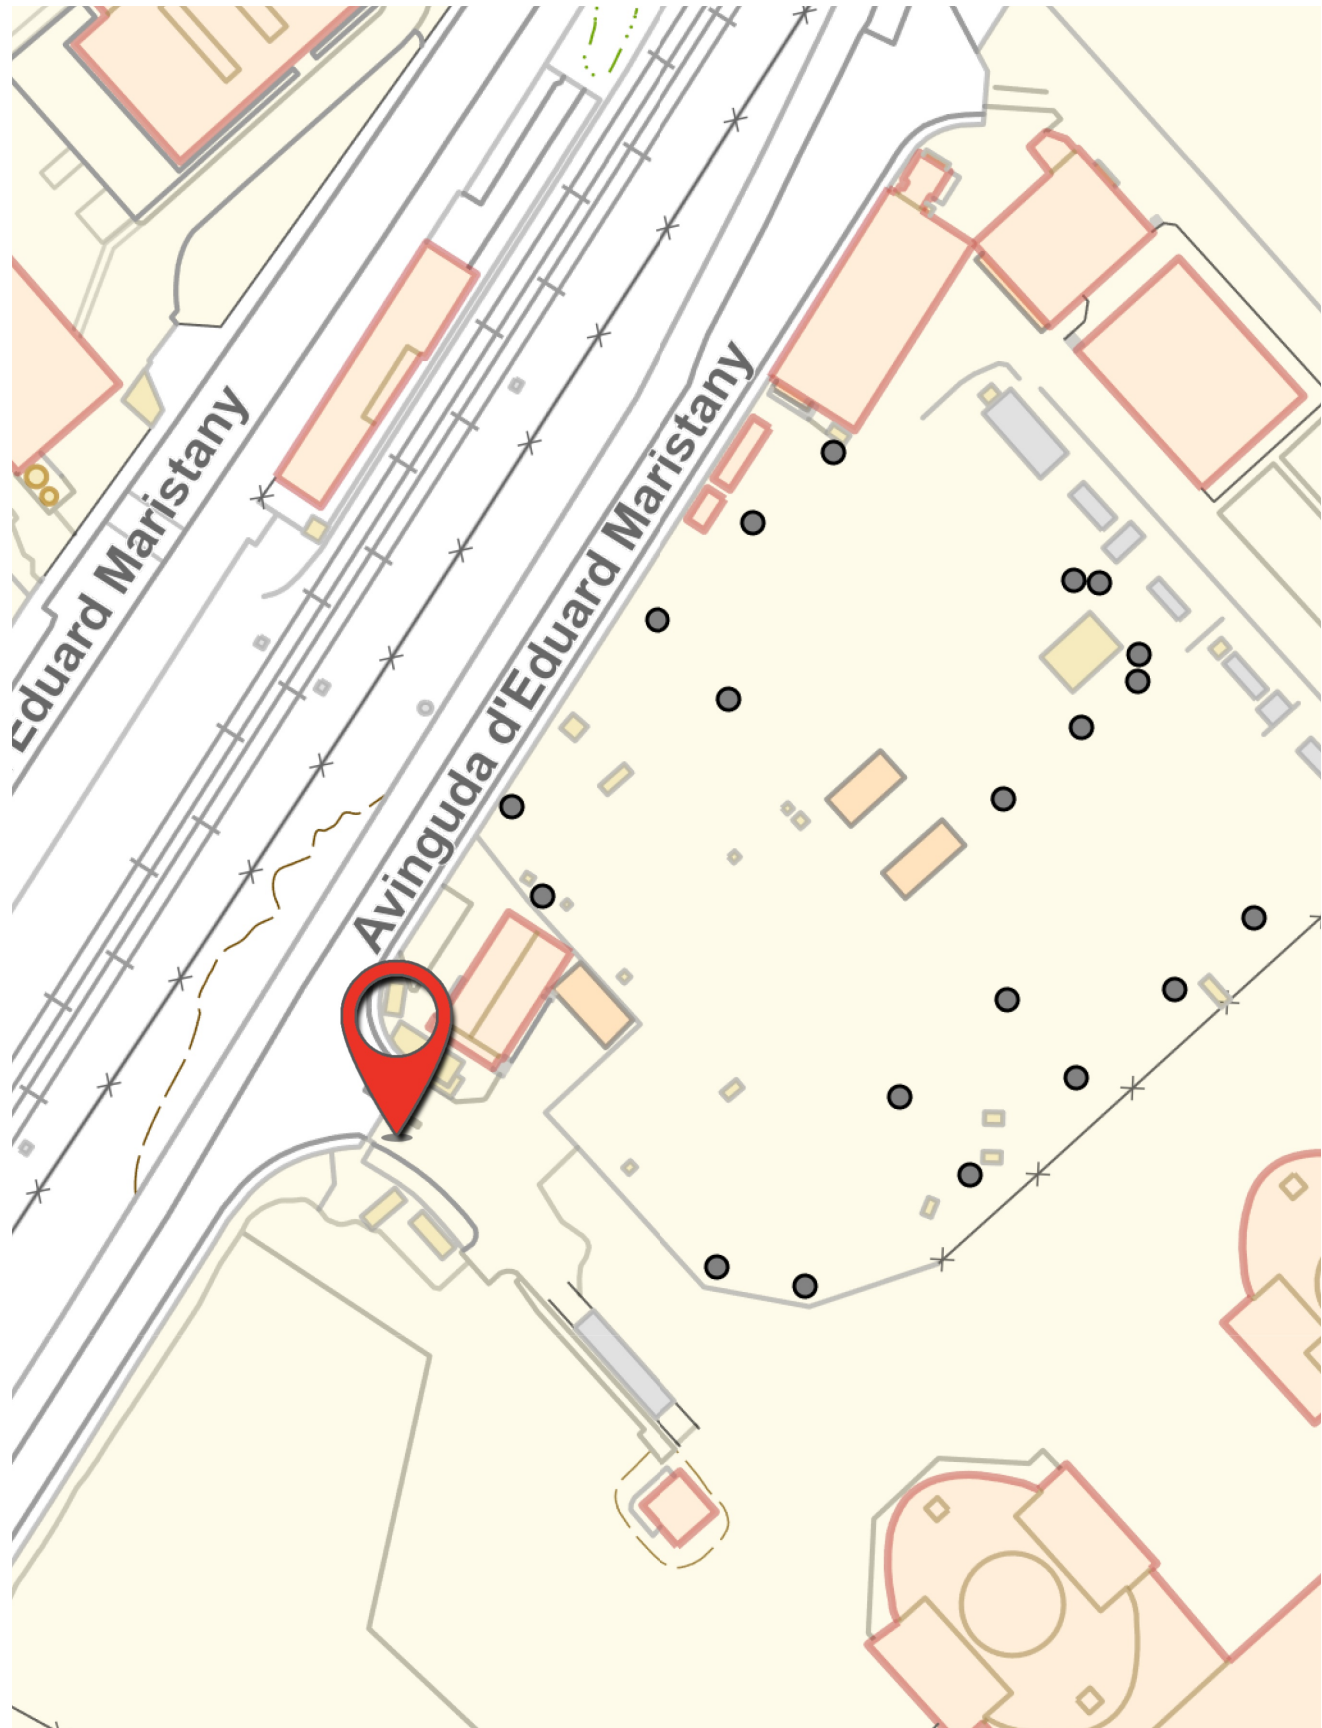

- 1 - Perfil quadrat metàl·lic acer galvanitzat de 15x15cm
- 2 - Sabata formigó 20x20cm
- 3 - Marc porta d'acer galvanitzat 2x2m
- 4 - Barrot metàl·lic acer galvanitzat de 3x3cm
- 5 - Pany de tancament amb clau
- 6 - Mur d'obra de fàbrica de maó de nova construcció (Detall MU-01)
- 7 - Nou quadre de telecomunicacions prefabricat de formigó 100x60cm
- 8 - Conduïte soterrat amb tub corrugat per pas cablejat Ø 5cm
- 9 - Tanca de torsió simple

